



FRONT-YARD OAK SAVANNA EDGE — Construction Details (Drawing 3 of 5)


DETAIL 1 — Stepping-Stone Path (scale ~1:8)

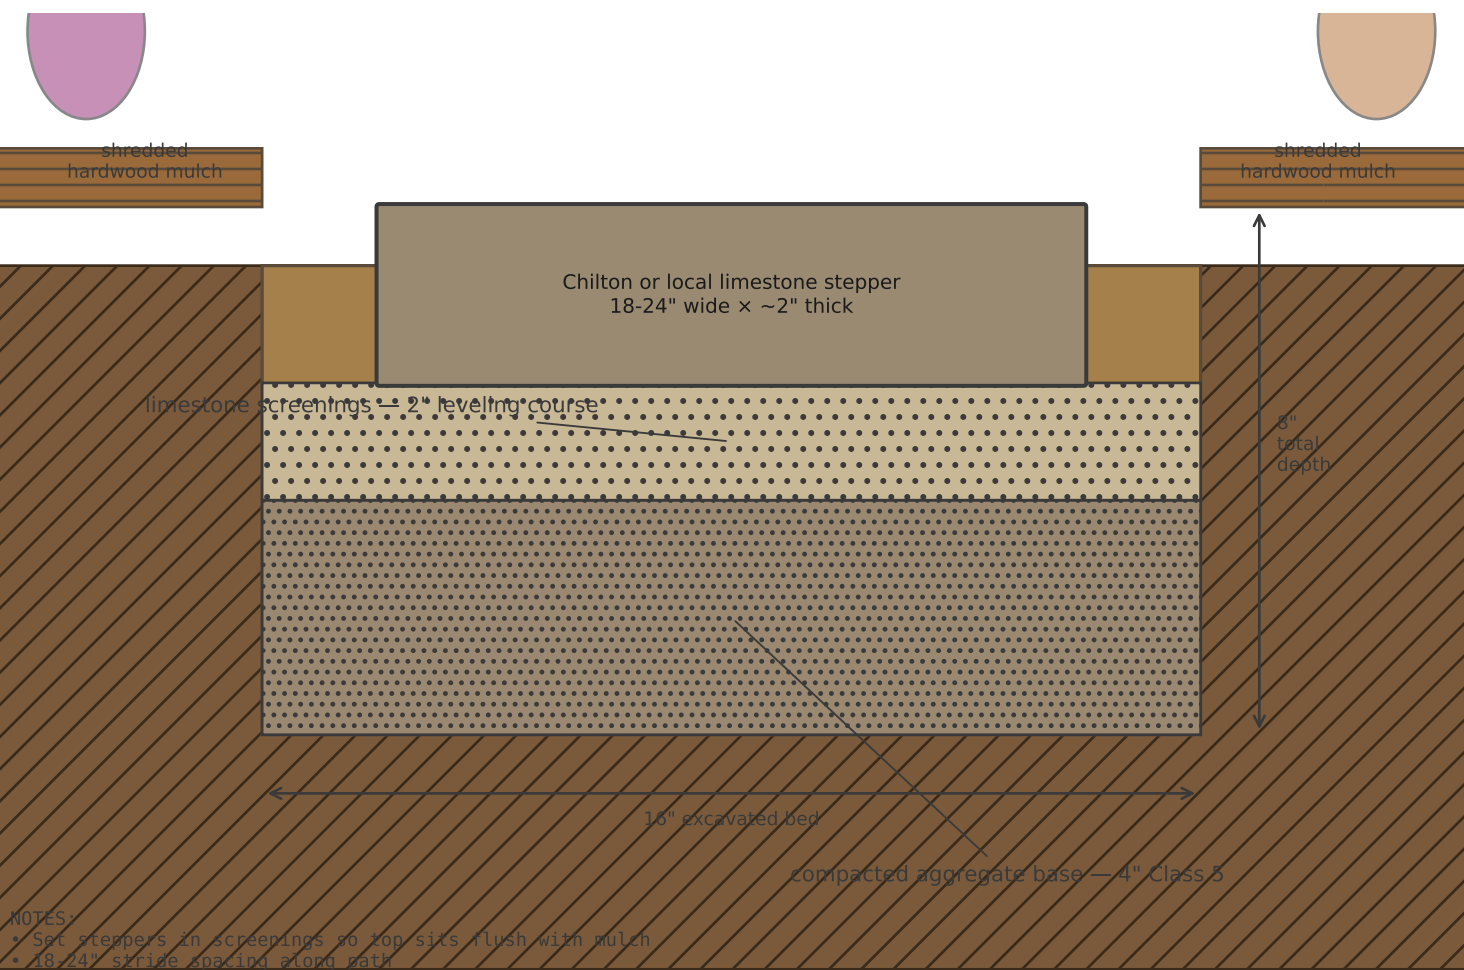

DETAIL 2 — Bench Pad (scale ~1:8)

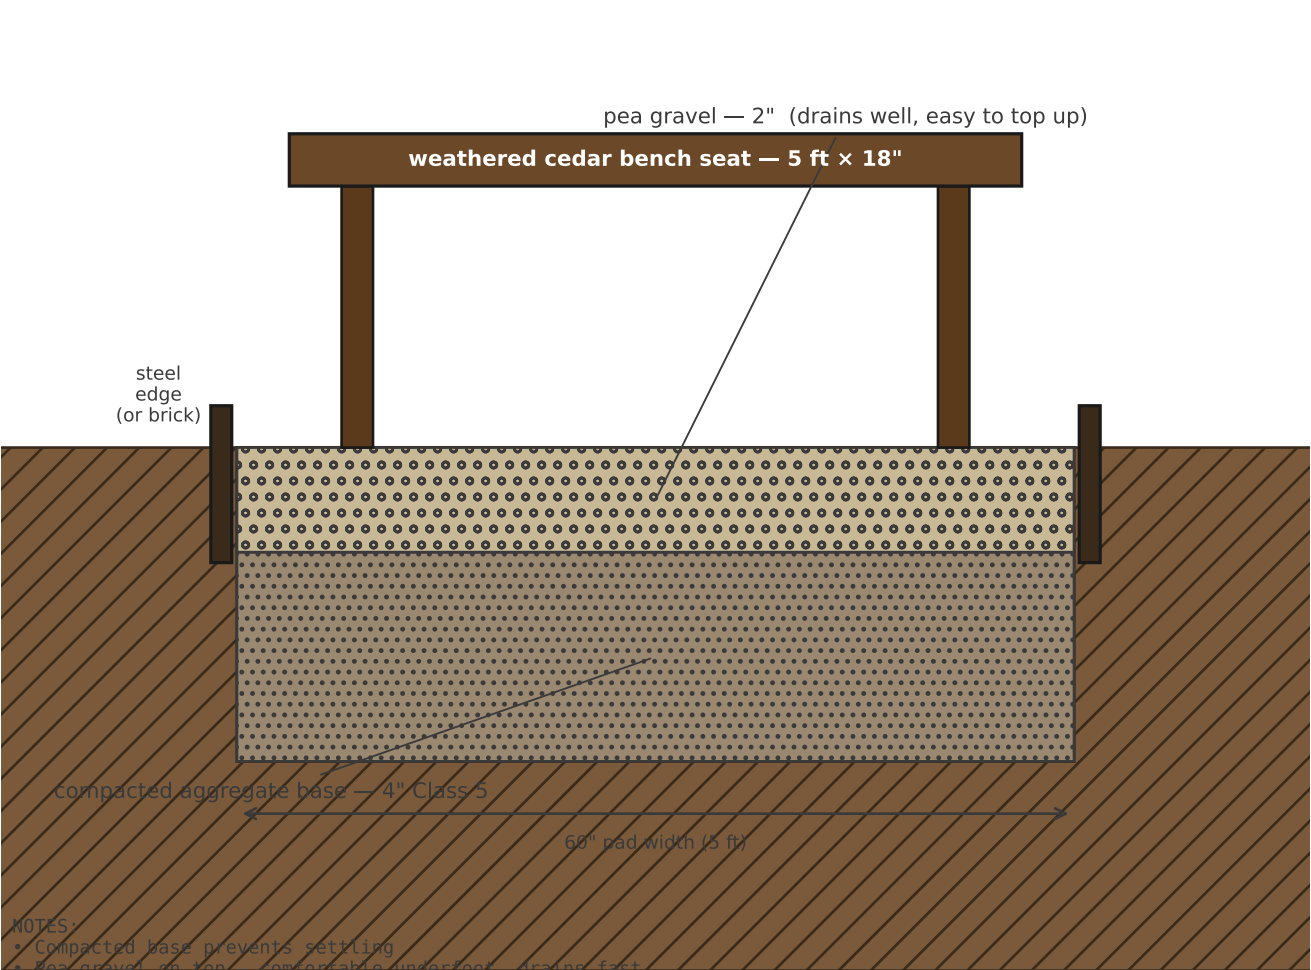

DETAIL 3 — Trench-Cut Bed Edge (scale ~1:4)

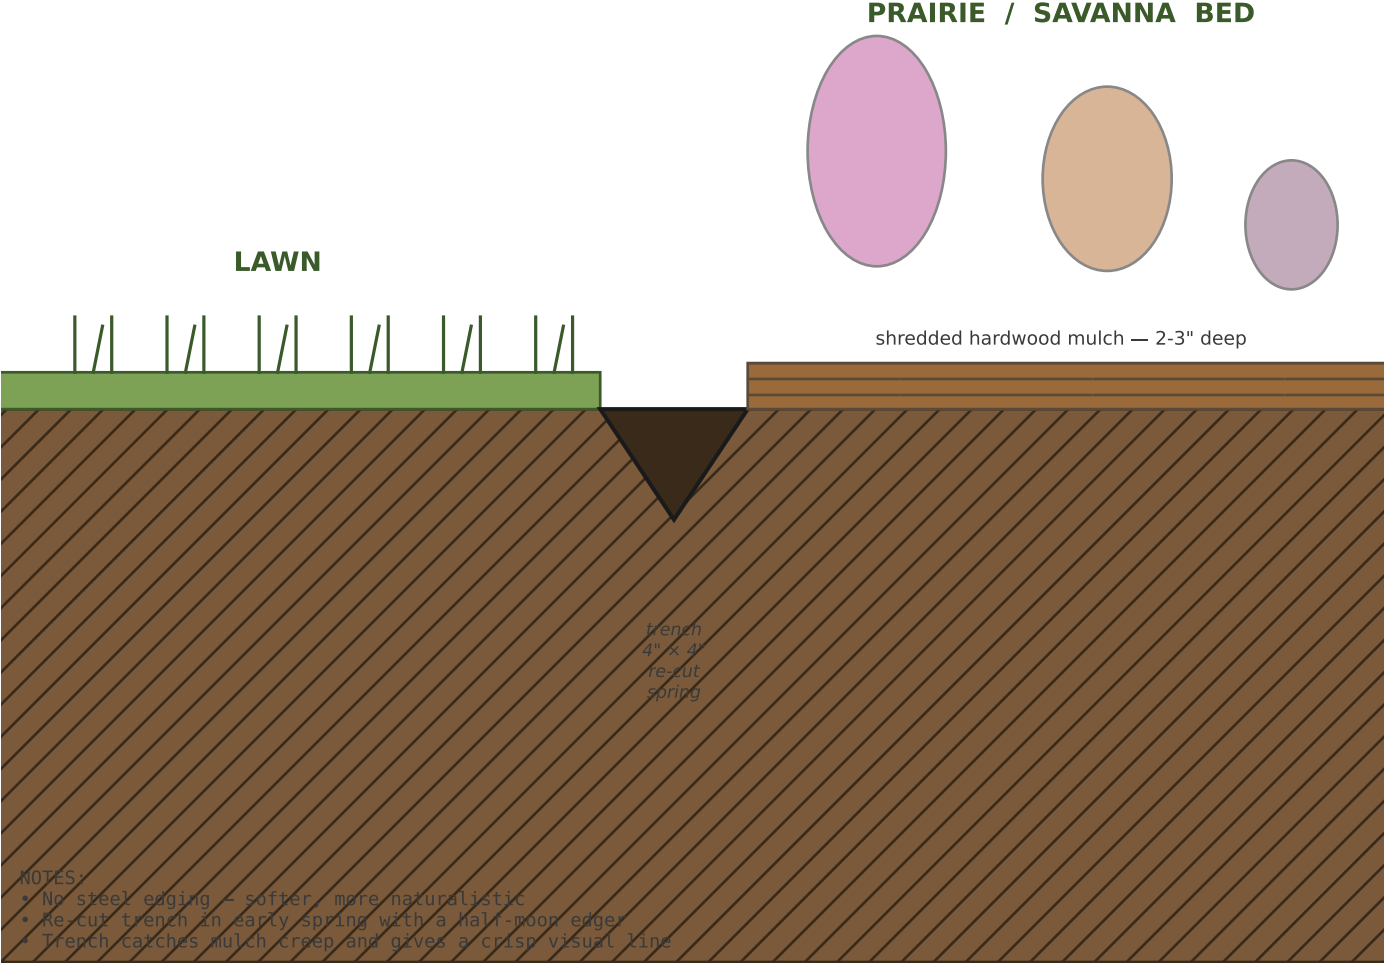

DETAIL 4 — Fieldstone Mowing Strip (alternative to trench edge — scale ~1:4)

